

100×20 м хайгуулын цооногийн санал, 1:5 000

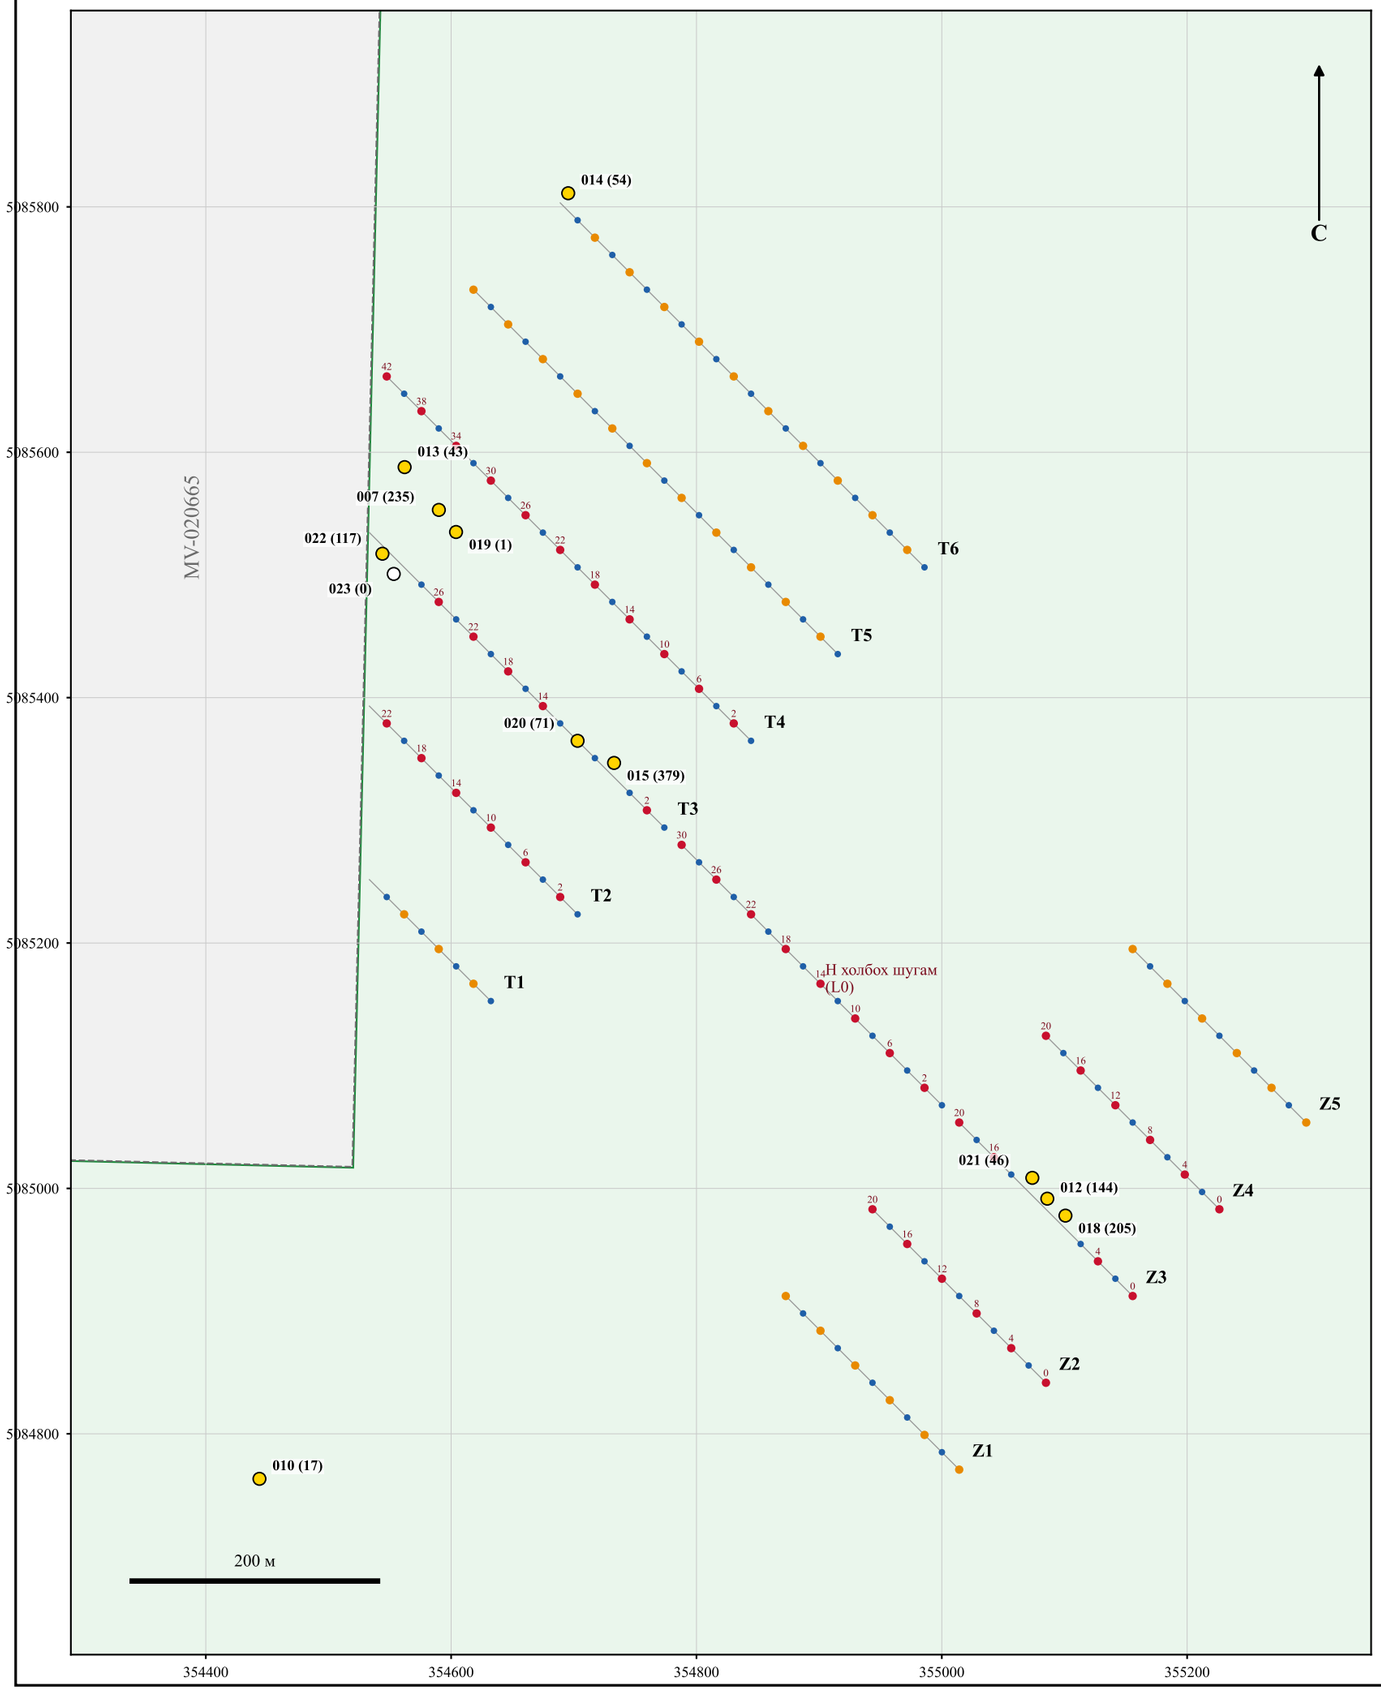

Талбайн тойм, 1:60 000

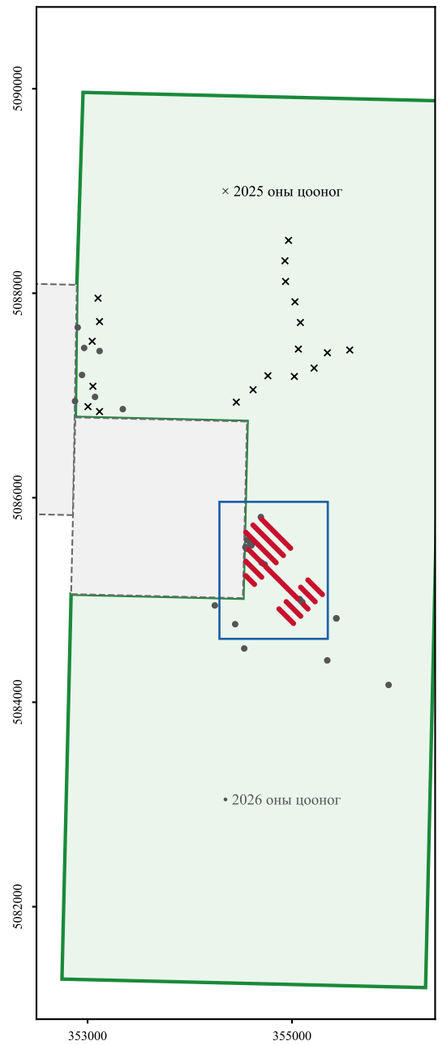

Цооногийн тоо

Ээлж	T	Z	H	Нийт	т/м 24.8 м	т/м 30 м
1-р ээлж	22	16	8	46	1,141	1,380
2-р ээлж	24	12	0	36	893	1,080
3-р ээлж	51	24	8	83	2,058	2,490
Нийт	**97**	**52**	**16**	**165**	**4,092**	**4,950**

Тайлбар

- 1-р ээлж: гол шугам, 40 м алхам
- 2-р ээлж: захын шугам, 40 м алхам
- 3-р ээлж: алт илэрвэл 20 м болгож нягтруулна
- 2026 оны цооног: алт илэрсэн (мг/м³ дээд дээж)
- 2026 оны цооног: алт илрээгүй эсвэл дээжгүй

Шугам аз 135°, хоорондоо 100 м, цооног 20 м.
T, Z дугаар нь шугамын дагуух дугаар (10 м-т 1).
Хилээс 10 м дотогш, 2026 оны цооногоос 12 м-ээс ойр зангилаанд цооног нэмээгүй.
Гүн: улаан хүрэн цул шаварт 2 м орсны дараа эсвэл 30 м-т зогсооно (геологич батална).

Хэсэг шугамын чиглэл нь 2026 оны цооног алтны утга, өндрийн налуугаар гаргасан санал. Газрын байдал, зам, урсгалыг газар дээр шалгаагүй. Эцсийн торлолыг шинжээчтэй тохирно.

Гүйцэтгэгч: **ГРИЙТ ВИШН ХХК**				*Аж үйлдвэр, эрдэс баялгийн яам Ашигт малтмал, газрын тосны газар Эрдэс баялгийн мэргэжлийн зөвлөл*	*Захиалагч:* *"ЭН СИ ЖИ ТИ" ХХК*	
А.туш	*Овог, нэр*	*Г.үсэг*	*Огноо*	*Говь-Алтай аймгийн Бигэр сумын нутагт орших XV-017716 тусгай зөвшөөрлийн талбайн алтны шороон хуримтлал*	*Цаасны хэмжээ*	*Масштаб*
Инженер	*Т.Дабааням*				*А3*	*1:5000*
Инженер	*Ч.Аръяабал*				*Нийт зураг: 1*	*Зураг: №1*
				Хайгуулын цооногийн төлөвлөгөөний зураг (100×20 м), санал	*Тусгай зөвшөөрлийн дугаар: XV-017716*	