

XV-017716 талбайн тойм, 1:40 000

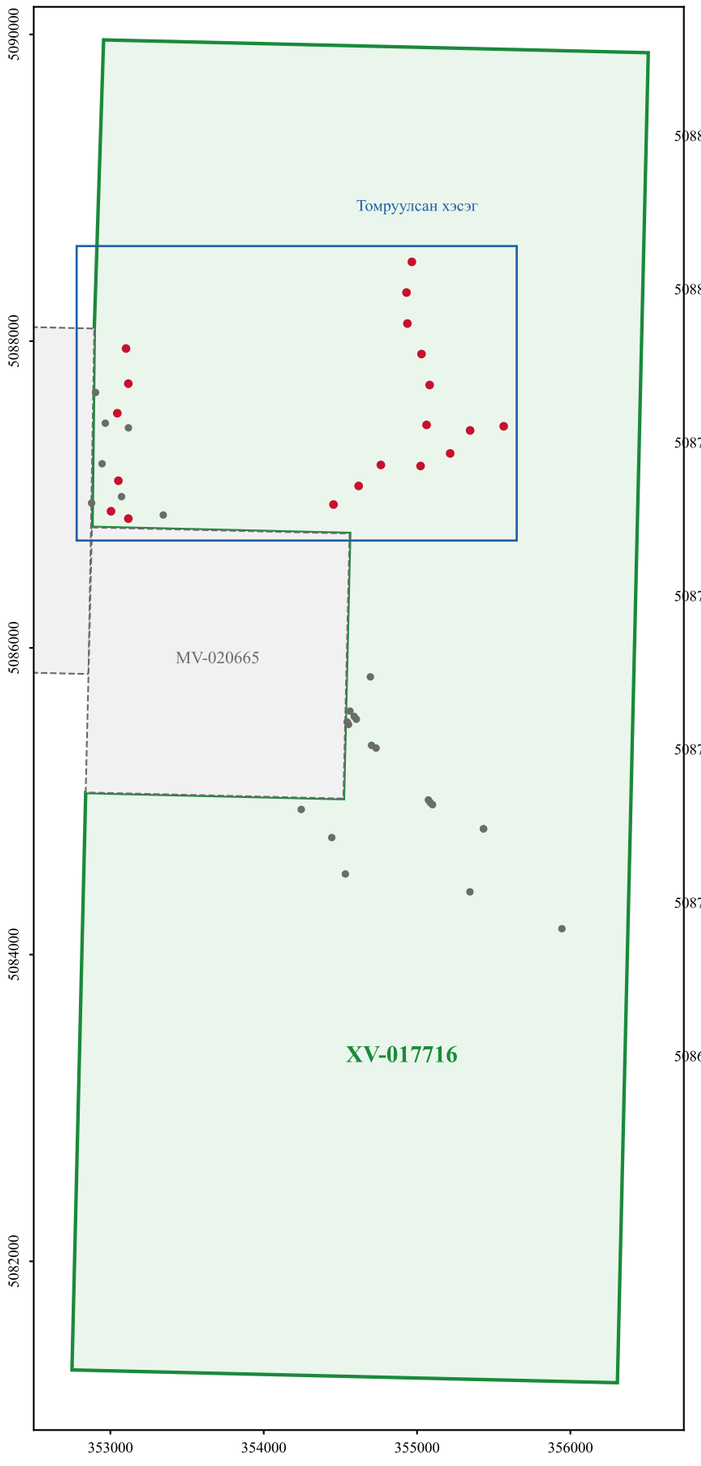

Талбайн булангууд: багцын shapefile, WGS84 UTM 47N.
Талбай 2 796 га (солбицлоор тооцов).
2025 оны 19 цооног бүгд XV-017716 дотор.
MV-020665, 17717, 15636 талбайд цооног ороогүй.

2025 оны цооногийн бодит байршил, 1:10 000

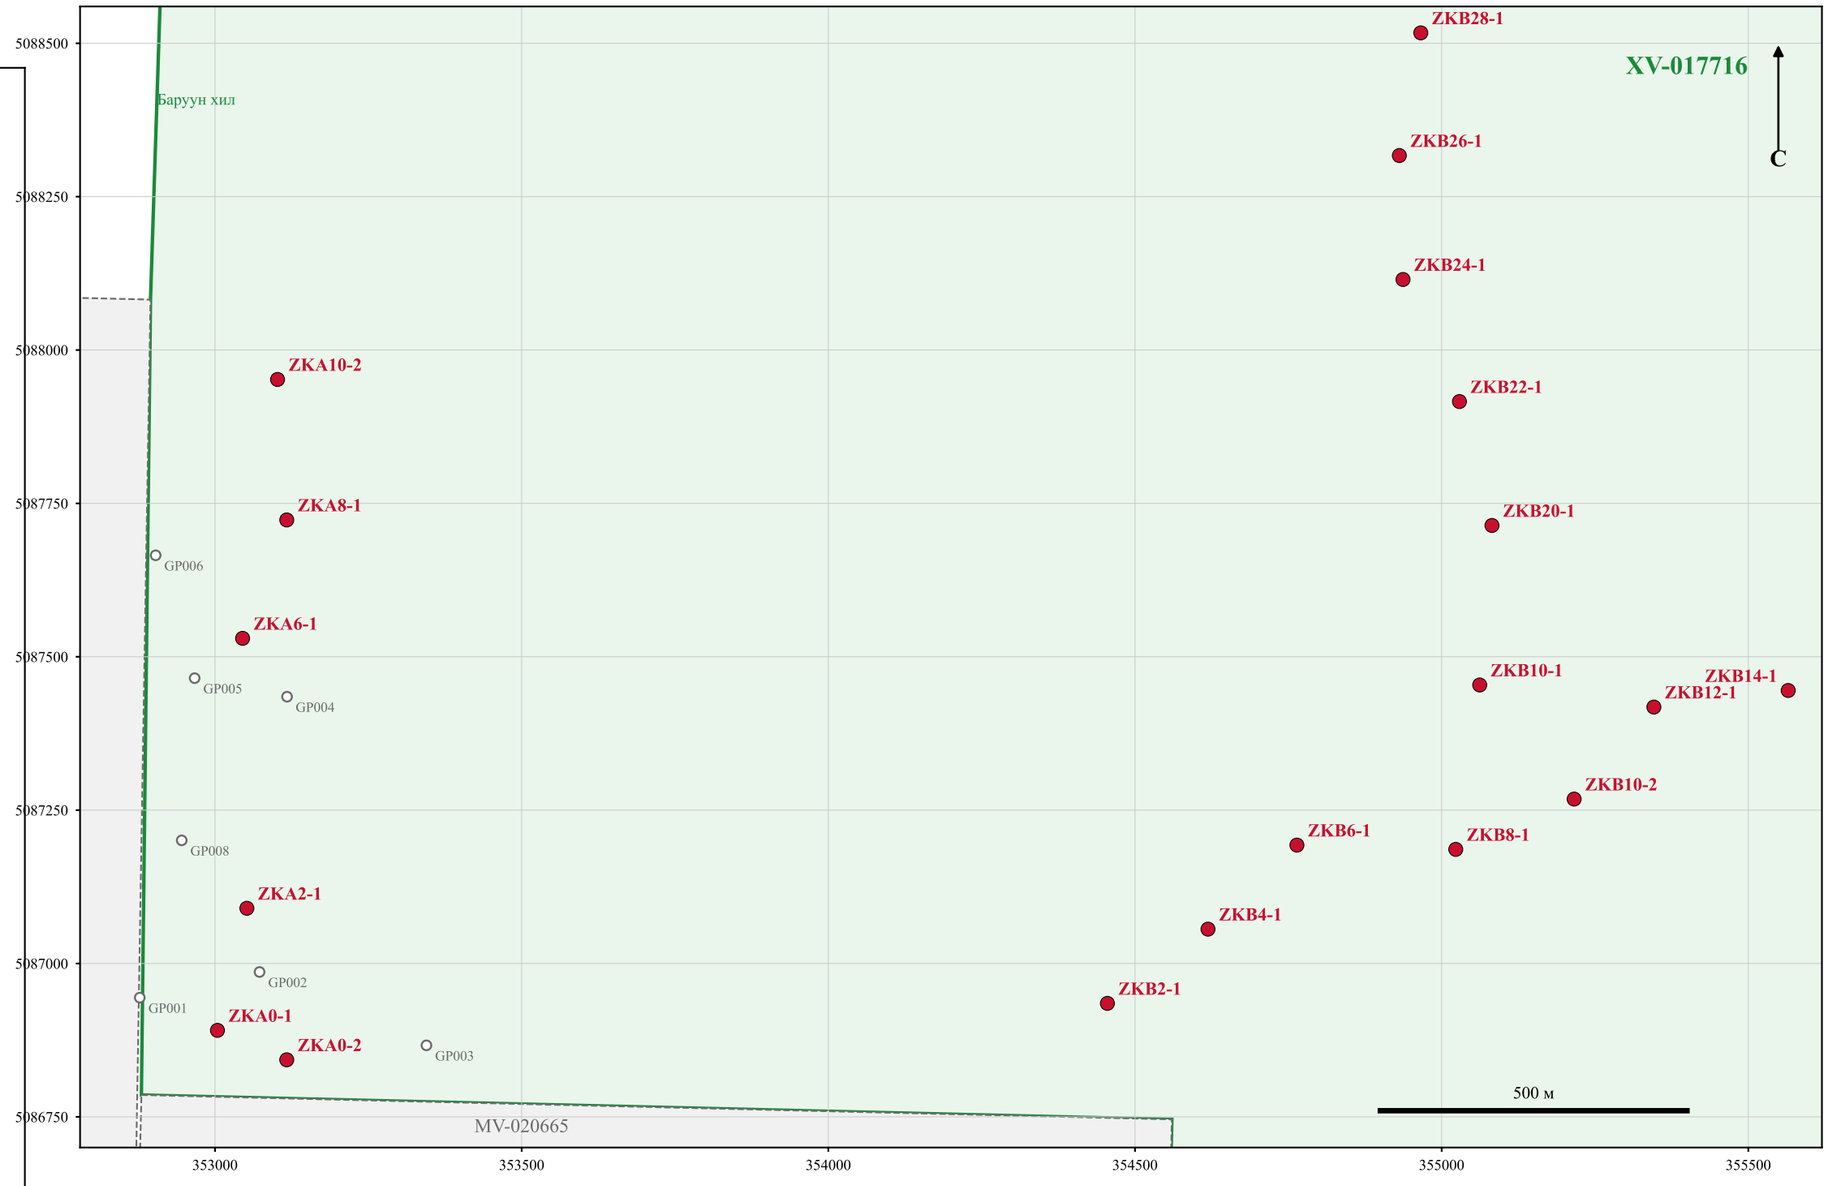

Цооног	Нээсэн	Хаасан	X	Y	Z	Гүн, м	Au, мг/м³
ZKA10-2	5.20	5.21	353102	5087952	1676	95.5	212
ZKA8-1	5.22	5.25	353117	5087723	1680	76.0	4
ZKA6-1	5.26	5.26	353045	5087530	1661	41.0	35
ZKA2-1	5.27	5.28	353052	5087090	1622	59.0	23
ZKA0-1	5.28	5.29	353004	5086891	1604	40.0	11
ZKA0-2	5.29	5.30	353117	5086843	1617	56.0	6
ZKB2-1	6.3	6.3	354455	5086935	1660	61.0	<10
ZKB4-1	6.4	6.5	354619	5087056	1662	61.0	<10
ZKB6-1	6.6	6.7	354764	5087193	1667	61.0	<10
ZKB10-1	6.8	6.8	355062	5087454	1715	61.0	<10
ZKB12-1	6.9	6.11	355346	5087418	1735	61.0	<10
ZKB10-2	6.12	6.12	355216	5087268	1734	61.0	40
ZKB8-1	6.13	6.14	355023	5087186	1698	52.0	90
ZKB20-1	6.15	6.15	355082	5087714	1754	61.0	<10
ZKB22-1	6.16	6.16	355029	5087916	1762	61.0	20
ZKB24-1	6.17	6.17	354937	5088115	1775	50.0	78
ZKB26-1	6.18	6.18	354931	5088317	1783	50.0	<10
ZKB28-1	6.19	6.19	354966	5088517	1792	40.0	<10
ZKB14-1	6.20	6.21	355565	5087445	1746	61.0	10
Нийт 19						**1108.5**	

Тайлбар

- 2025 оны цооног (19, 1 108.5 м, 5-р сарын 20-6-р сарын 21)
- 2026 оны УКС цооног (25)
- XV-017716 тусгай зөвшөөрөл (тасархай: NCGT-ийн бусад талбай)

Солбицол, огноо, гүн: 2025 оны логийн толгой, 1 м-ээр тоймлосон. Au: цооногийн хамгийн өндөр дээж. ZKA логийн ихэнх дээжид утга «-», ZKB логийд «<0.01 г/м³». Логийн гарчгийн «Хуурай талбай» нь нэр, байршлыг солбицлоор шалгав. Газар дээр хэмжээгүй.

Гүйцэтгэгч: **ГРИЙТ ВИШН ХХК**				*Аж үйлдвэр, эрдэс баялгийн яам Ашигт малтмал, газрын тосны газар Эрдэс баялгийн мэргэжлийн зөвлөл*	*Захиалагч:* *"ЭН СИ ЖИ ТИ" ХХК*
А.туш	*Овог, нэр*	*Г.үсэг*	*Огноо*	*Говь-Алтай аймгийн Бигэр сумын нутагт орших XV-017716 тусгай зөвшөөрлийн талбайн алтны шороон хуримтлал*	*Цаасны хэмжээ:* *А3* / *Масштаб:* *1:10000*
Инженер	*Т.Дававаням*				*Нийт зураг: 1* / *Зураг: №1*
Инженер	*Ч.Аръяабал*				
				2025 оны өрөмдлөгийн цооногийн бодит байршлын зураг	*Тусгай зөвшөөрлийн дугаар: XV-017716*