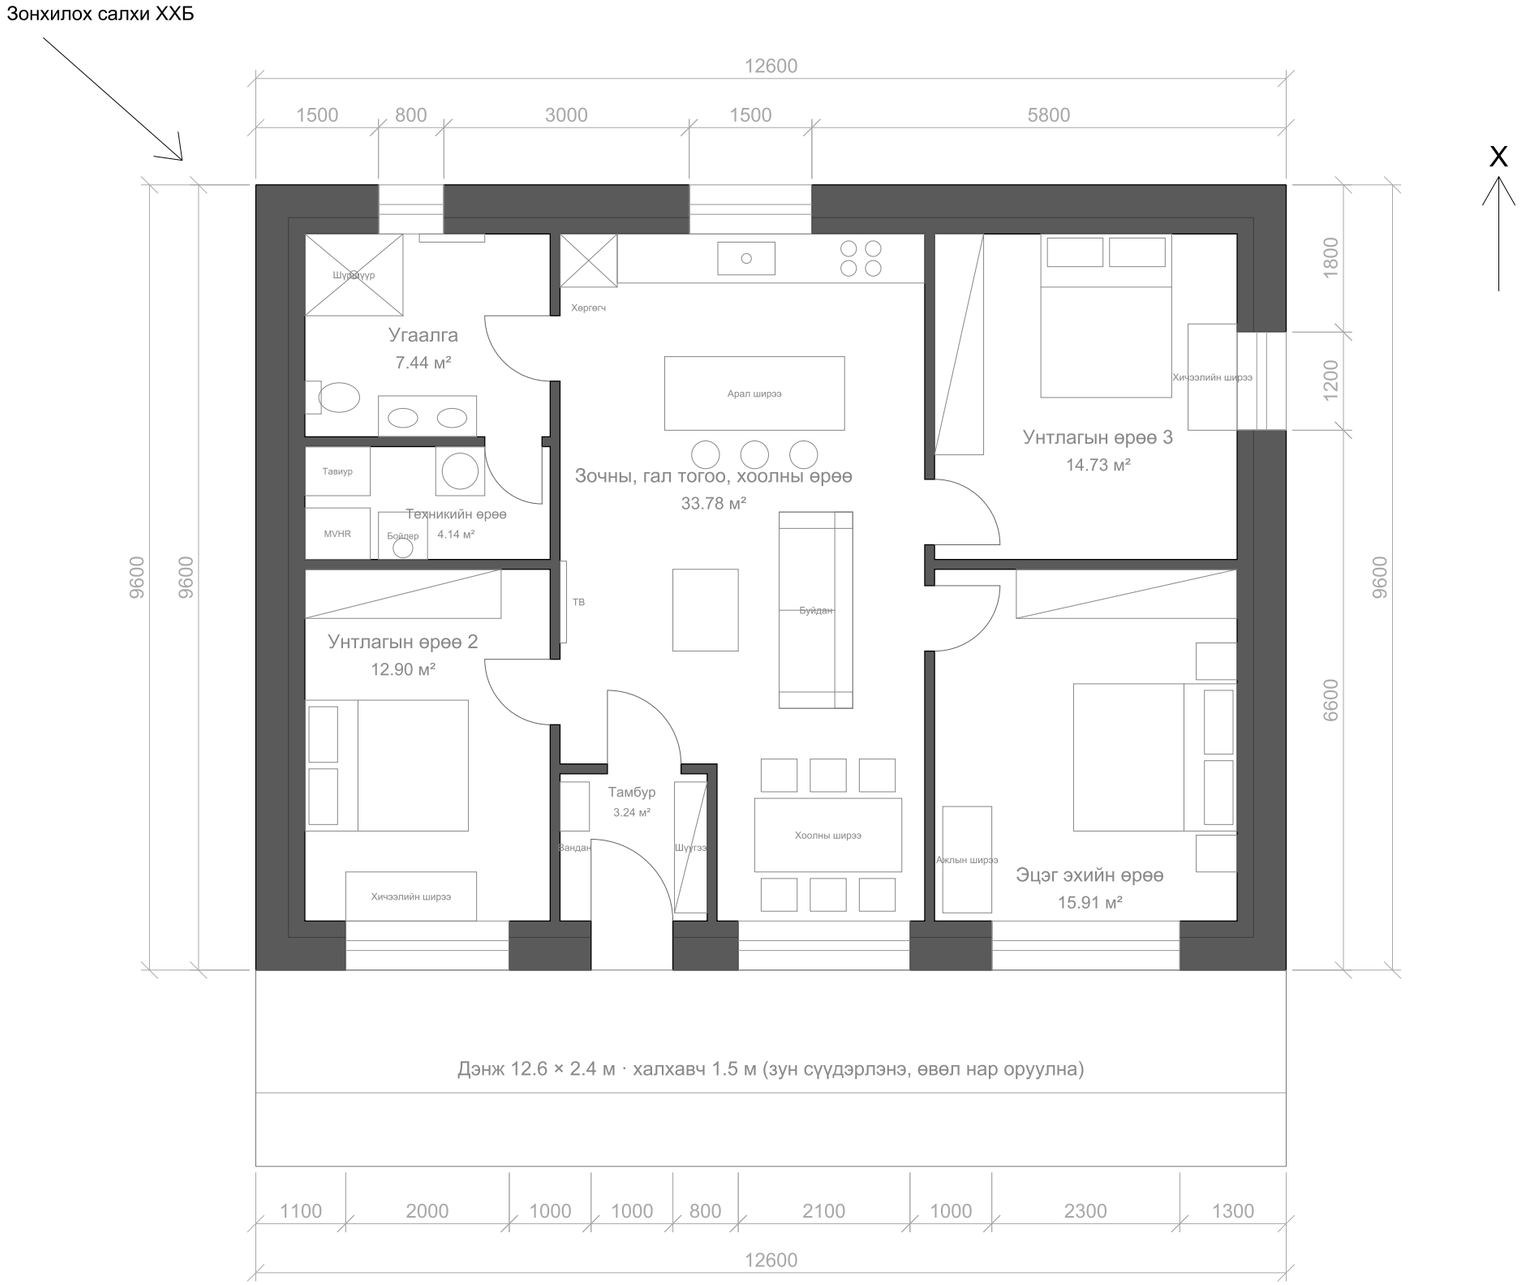


Санал D · Пассив байшин, нар-салхинд тааруулсан · Тавилгатай план M 1:75

Гадна 12.6 × 9.6 м = 121.0 м² · Ашигтай 92.1 м² (76 %) · Коридоргүй · Гадна хана 600 (блок 200 + дулаалга 400), дотор 120 мм